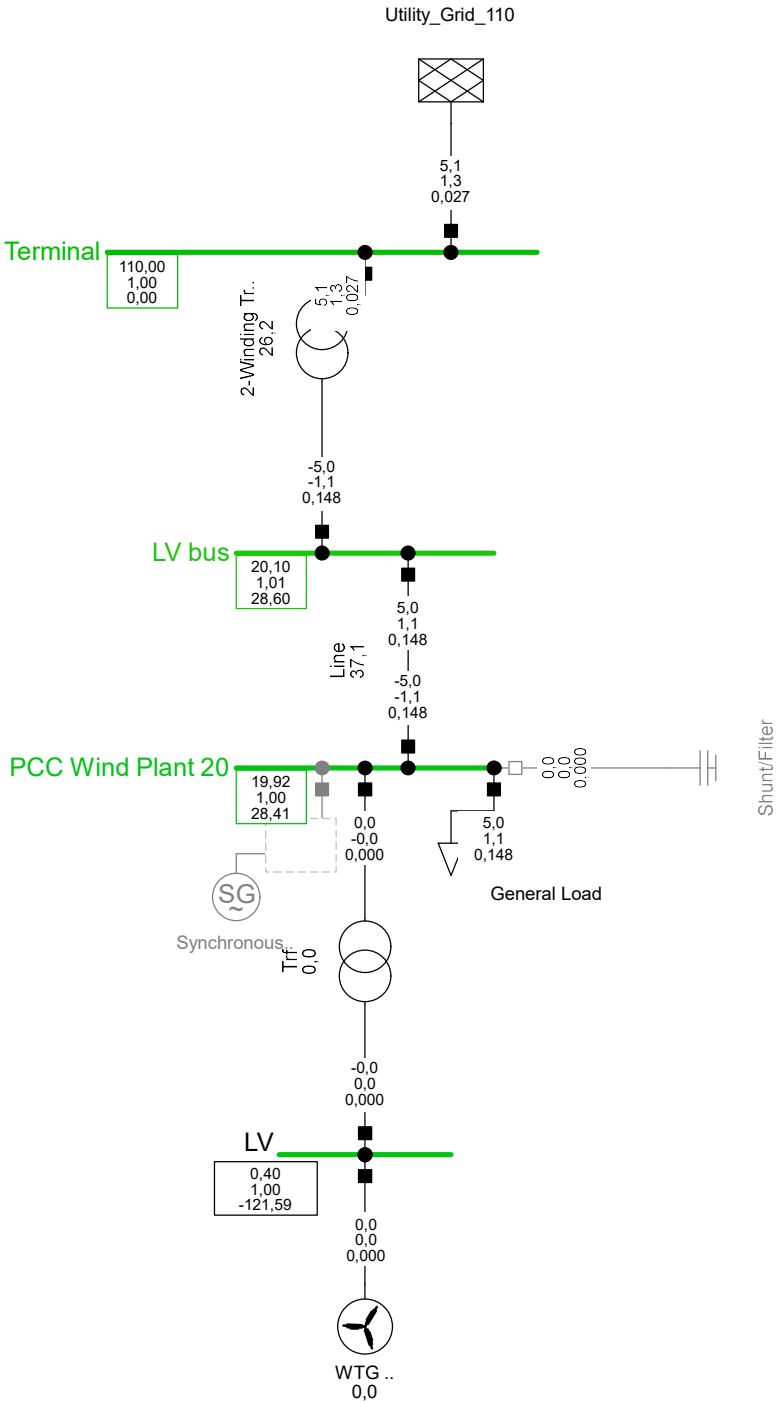

Utility_Grid_110
5,1
1,3
0,027
Terminal
110,00
1,00
0,00
2-Winding Tr..
26,2
5,1
1,3
0,027
-5,0
-1,1
0,148
LV bus
20,10
1,01
28,60
5,0
1,1
0,148
Line
37,1
-5,0
-1,1
0,148
PCC Wind Plant 20
19,92
1,00
28,41
0,0
0,0
0,000
Shunt/Filter
0,0
-0,0
0,000
5,0
1,1
0,148
General Load
SG
Synchronous..
Trf
0,0
-0,0
0,0
0,000
LV
0,40
1,00
-121,59
0,0
0,0
0,000
WTG ..
0,0