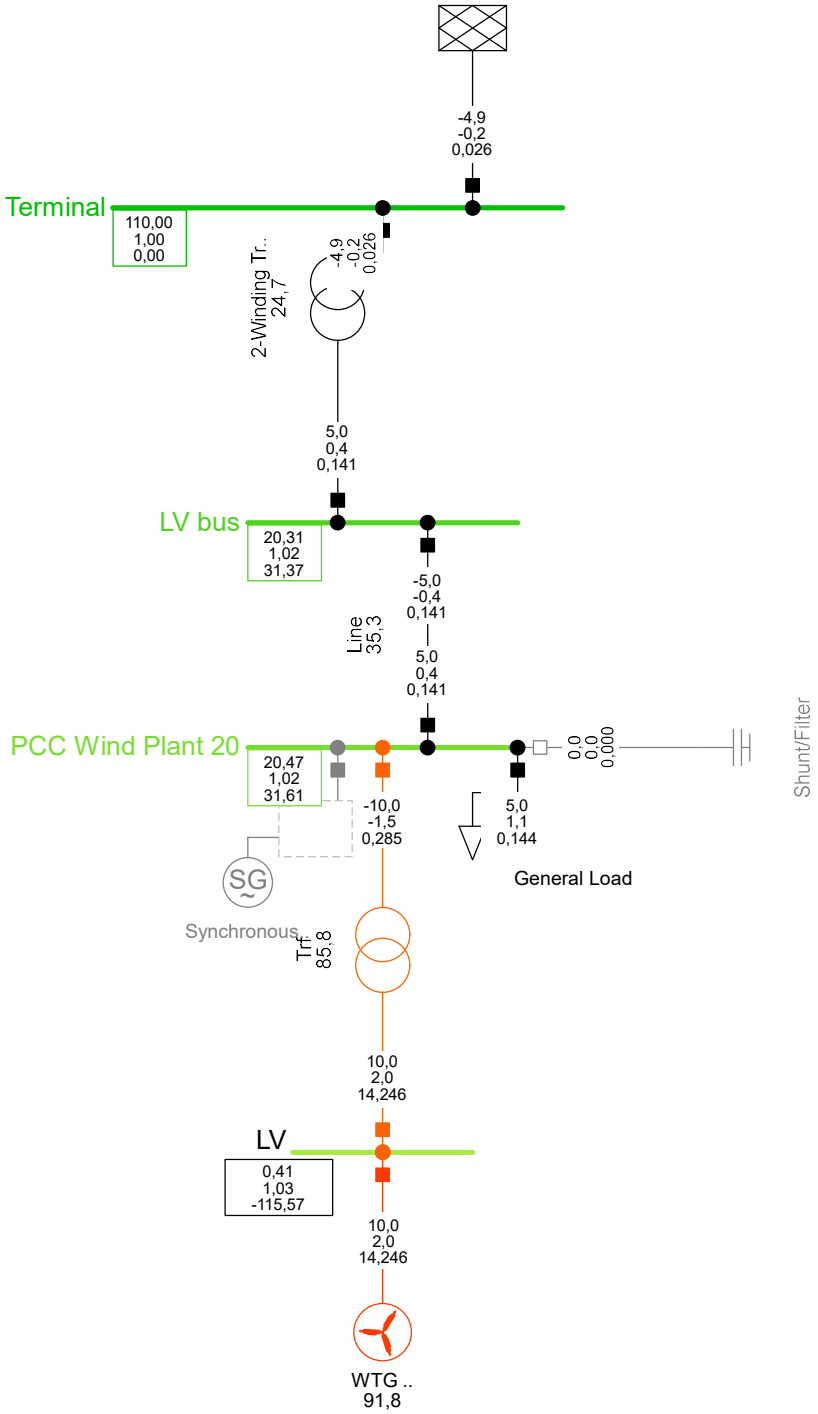

-4,9
-0,2
0,026
Terminal
110,00
1,00
0,00
2-Winding Tr..
24,7
-4,9
-0,2
0,026
5,0
0,4
0,141
LV bus
20,31
1,02
31,37
-5,0
-0,4
0,141
Line
35,3
5,0
0,4
0,141
PCC Wind Plant 20
20,47
1,02
31,61
0,0
0,0
0,000
Shunt/Filter
-10,0
-1,5
0,285
5,0
1,1
0,144
General Load
SG
Synchronous
Trf.
85,8
10,0
2,0
14,246
LV
0,41
1,03
-115,57
10,0
2,0
14,246
WTG ..
91,8